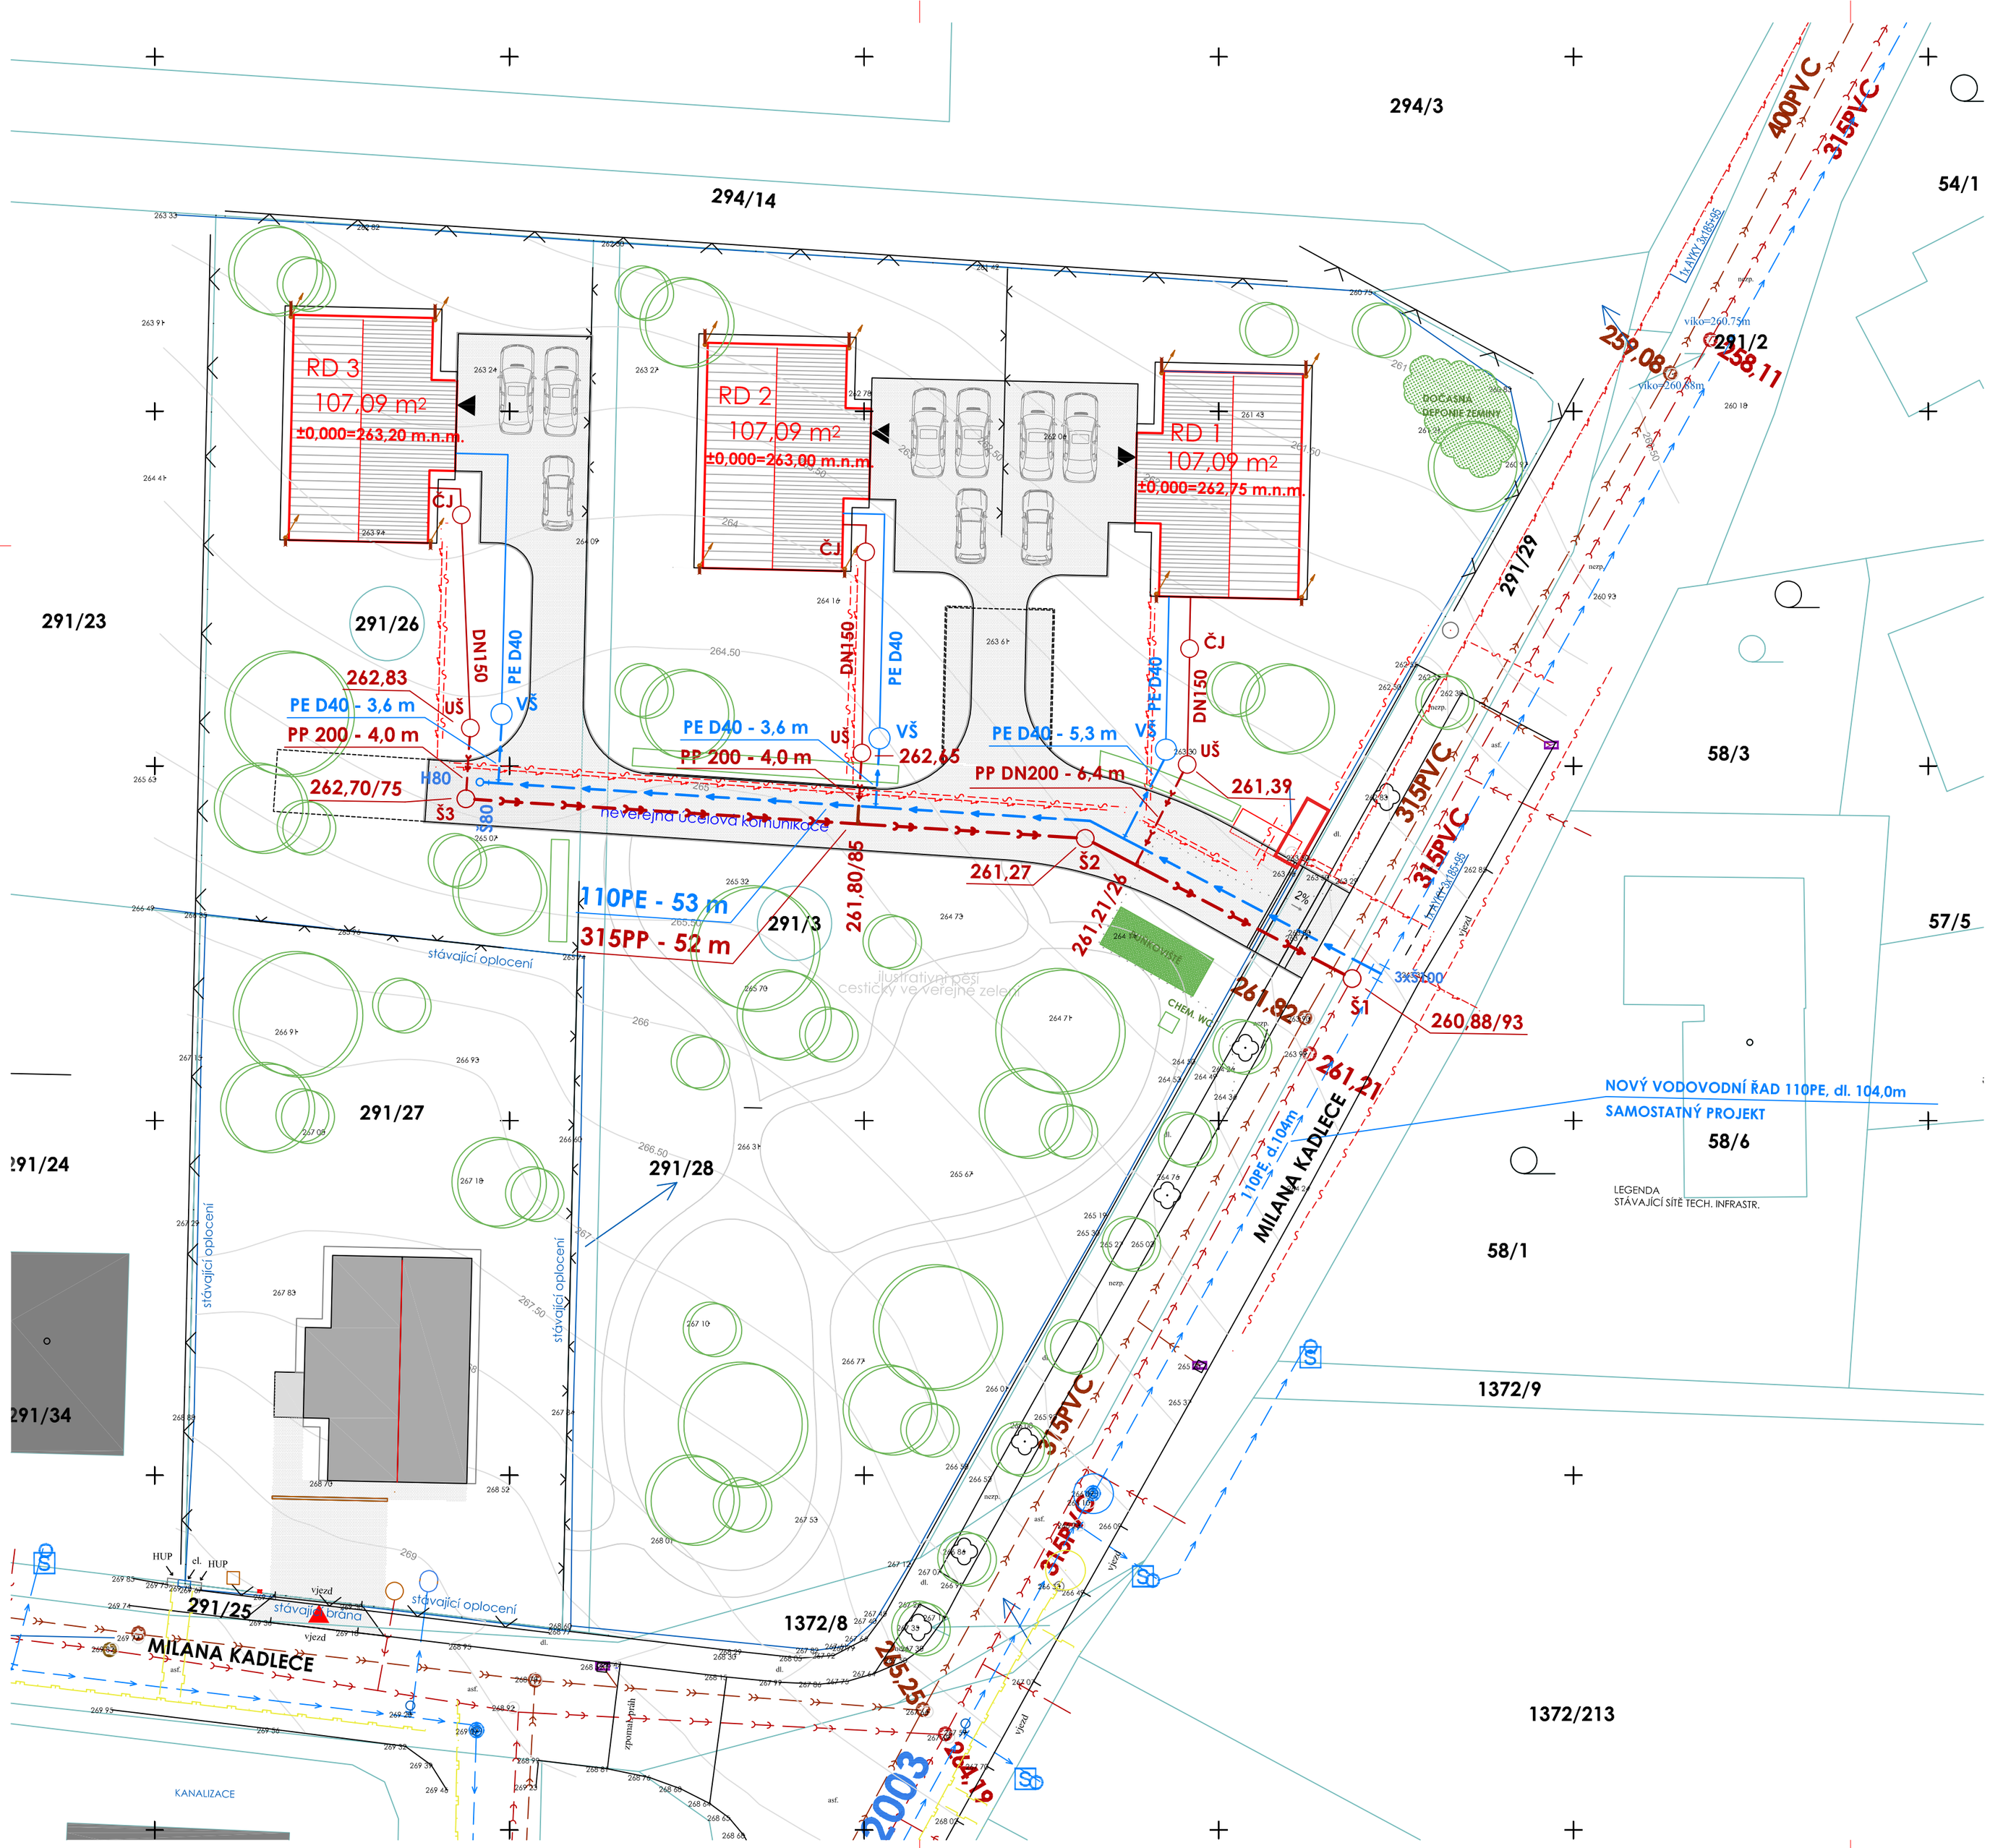

LEGENDA:

stávající sítě

- VODOVOD
- SPLAŠKOVÁ KANALIZACE
- DEŠŤOVÁ KANALIZACE

navržené sítě

- VODOVODNÍ ŘAD
- VODOVODNÍ PŘÍPOJKA
- DOMOVNÍ VODOVOVOD
- STOKA SPLAŠKOVÉ KANALIZACE
- PŘÍPOJKA SPLAŠKOVÉ KANALIZACE
- DOMOVNÍ SPLAŠKOVÁ KANALIZACE

Generální projektant:	**STUDIO AM s.r.o.** Na Bojišti 1470/24, Praha 2 -Nové Město, 120 00
Zodpovědný projektant:	Ing. Mojmír Hnilica **Ke Zděři 364/7, 153 00 Praha 16**
Projektant:	**Ing. Mojmír Hnilica**
Investor:	**Softel Consulting s.r.o.** Ocelkova 643/20, 198 00 Praha 9
Název projektu:	**NOVOSTAVBA 3RD** parc.č. 291/26, 291/28, 291/29, 291/3, k.ú. DOLNÍ CHABRY
Stupeň dokumentace:	**DOKUMENTACE PRO POVOLENÍ ZÁMĚRU**
Výkres:	SITUACE
Část dokumentace:	VODOVOD, KANALIZACE — D.5 — Č. výkresu: 2
Datum:	**ZÁŘÍ 2025** — Měřítko: 1:250 — Formát: 6 A4 — Číslo paré: